

Bestands Abgesch erklärung

Eigentümer: Ludwig
Badstra
86 7


Bauort: Fl.Nr.
Donauw
86154

Anerkannt: _____


Grundris
Schnitte
Ansichte

Ostans

Gefertigt: 20.09.1994
Der Planverfasser:

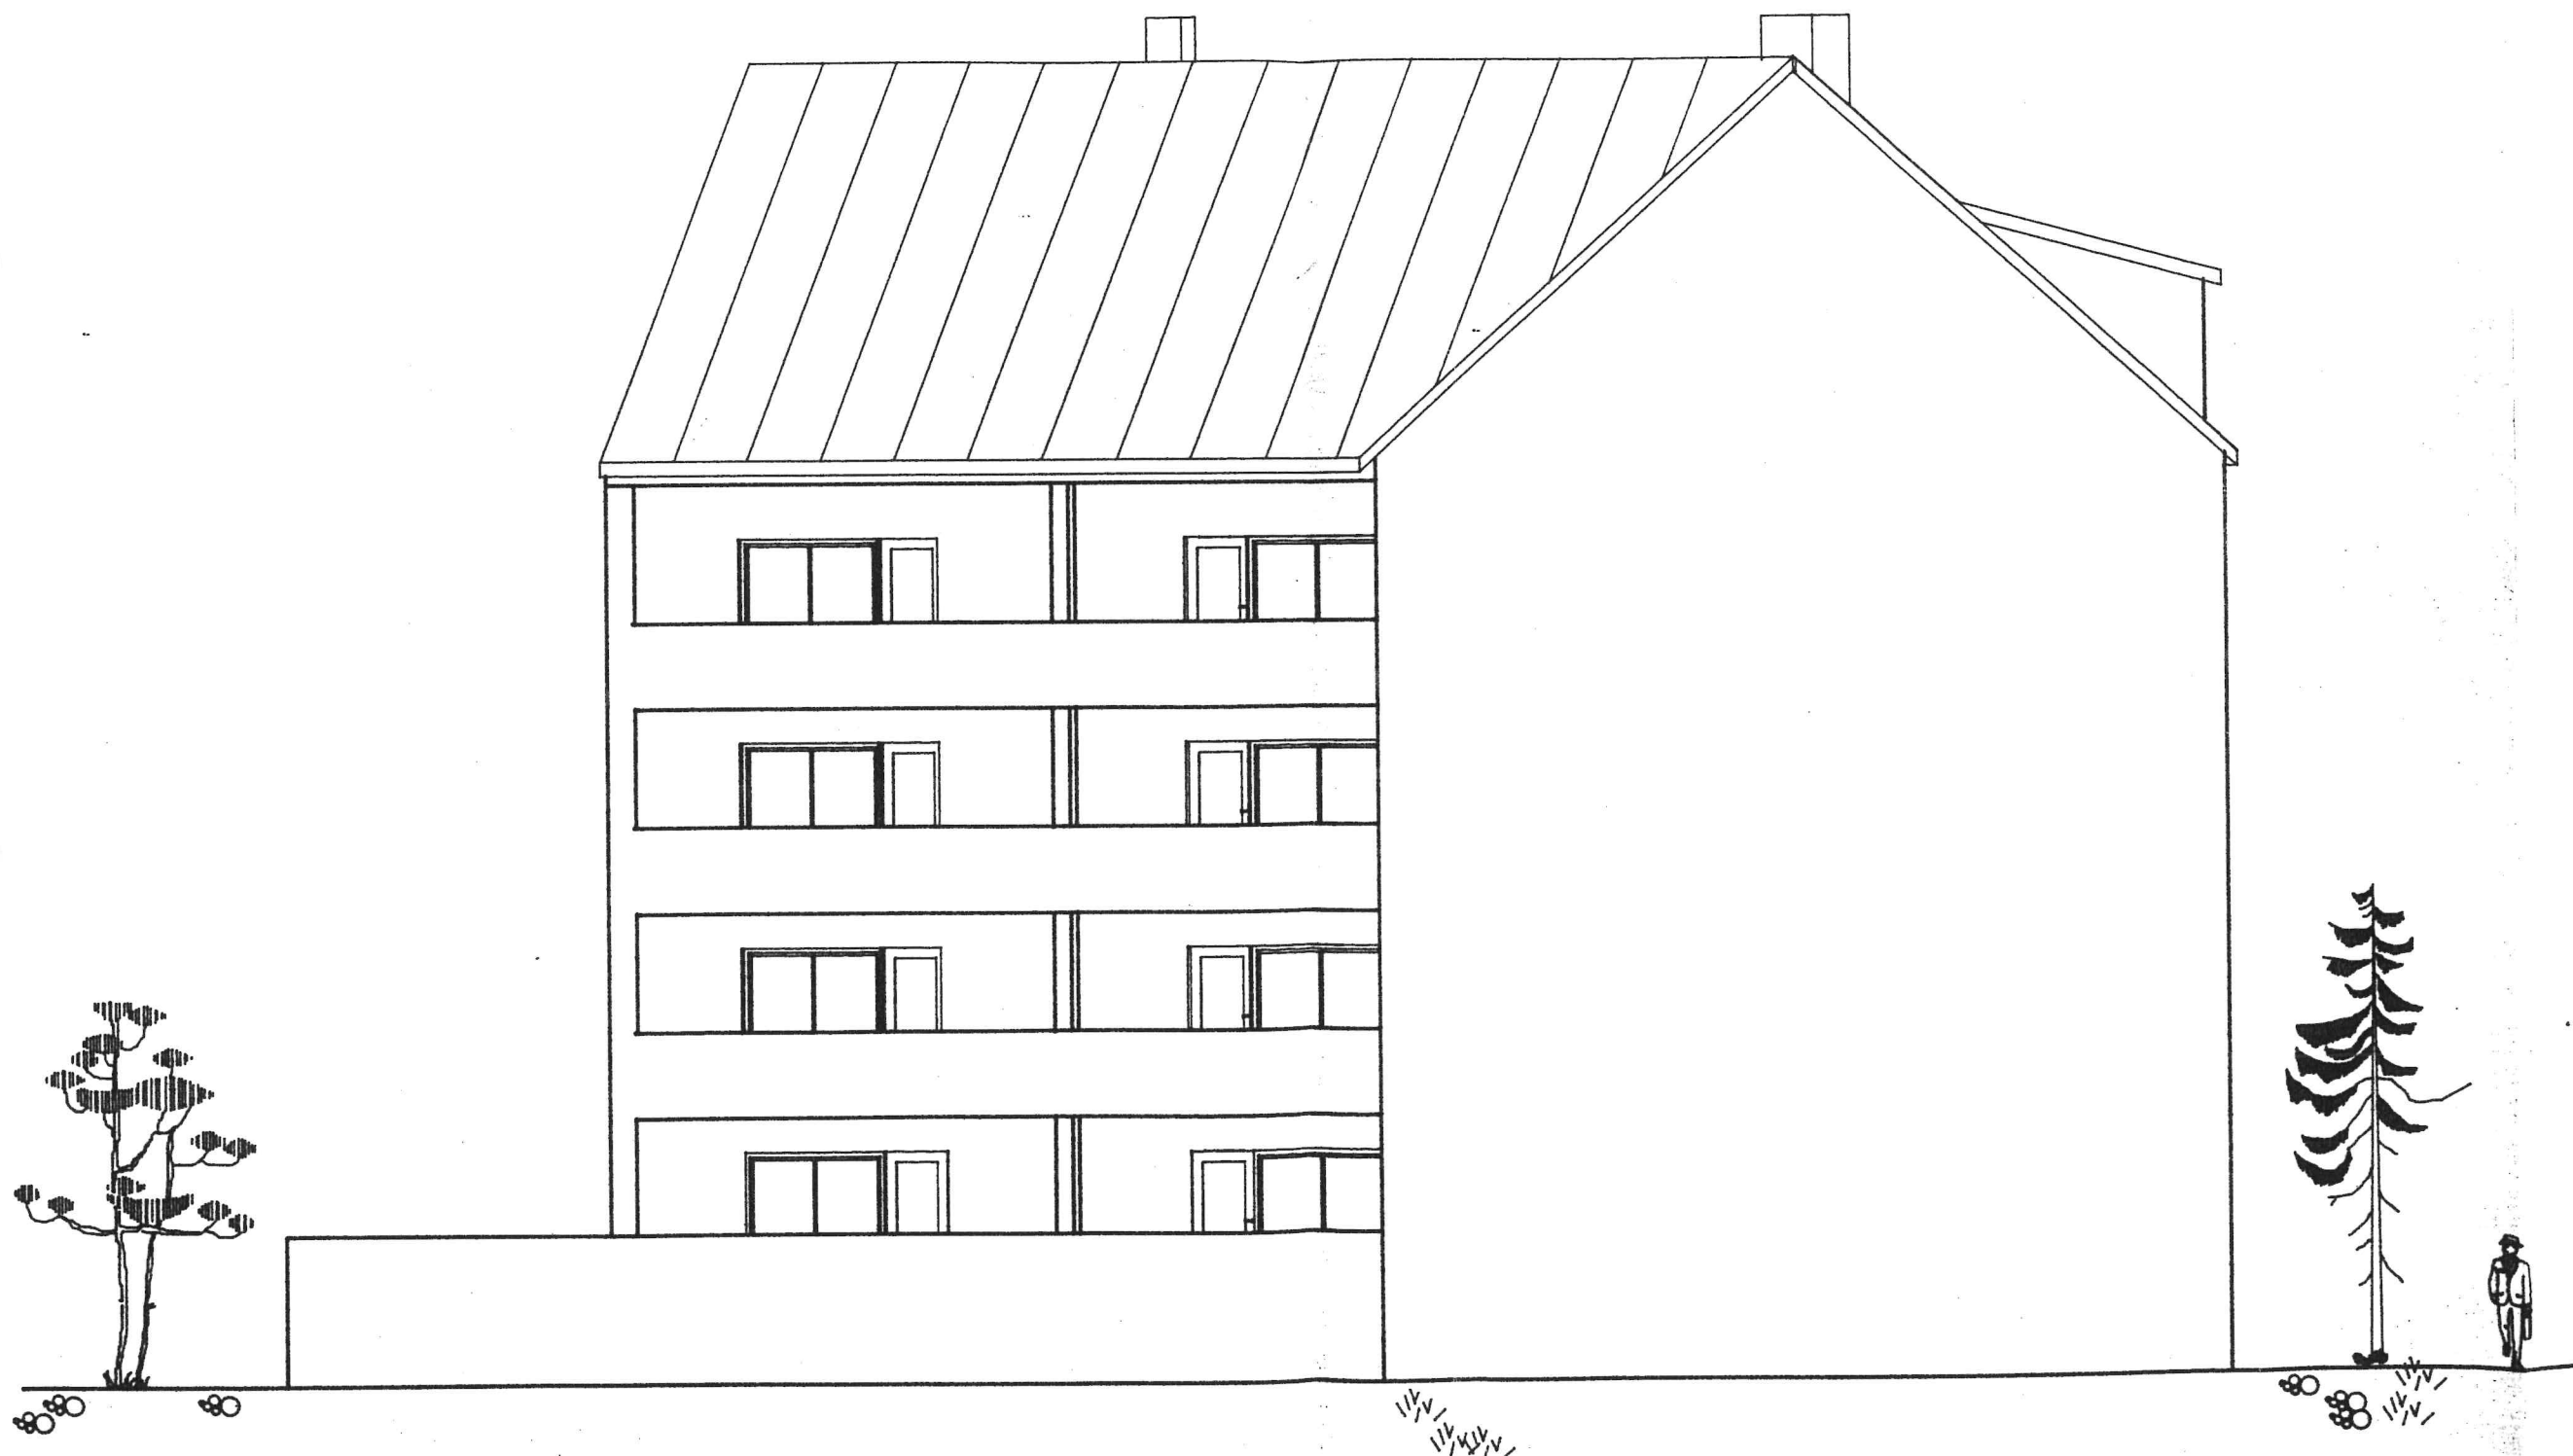

FW

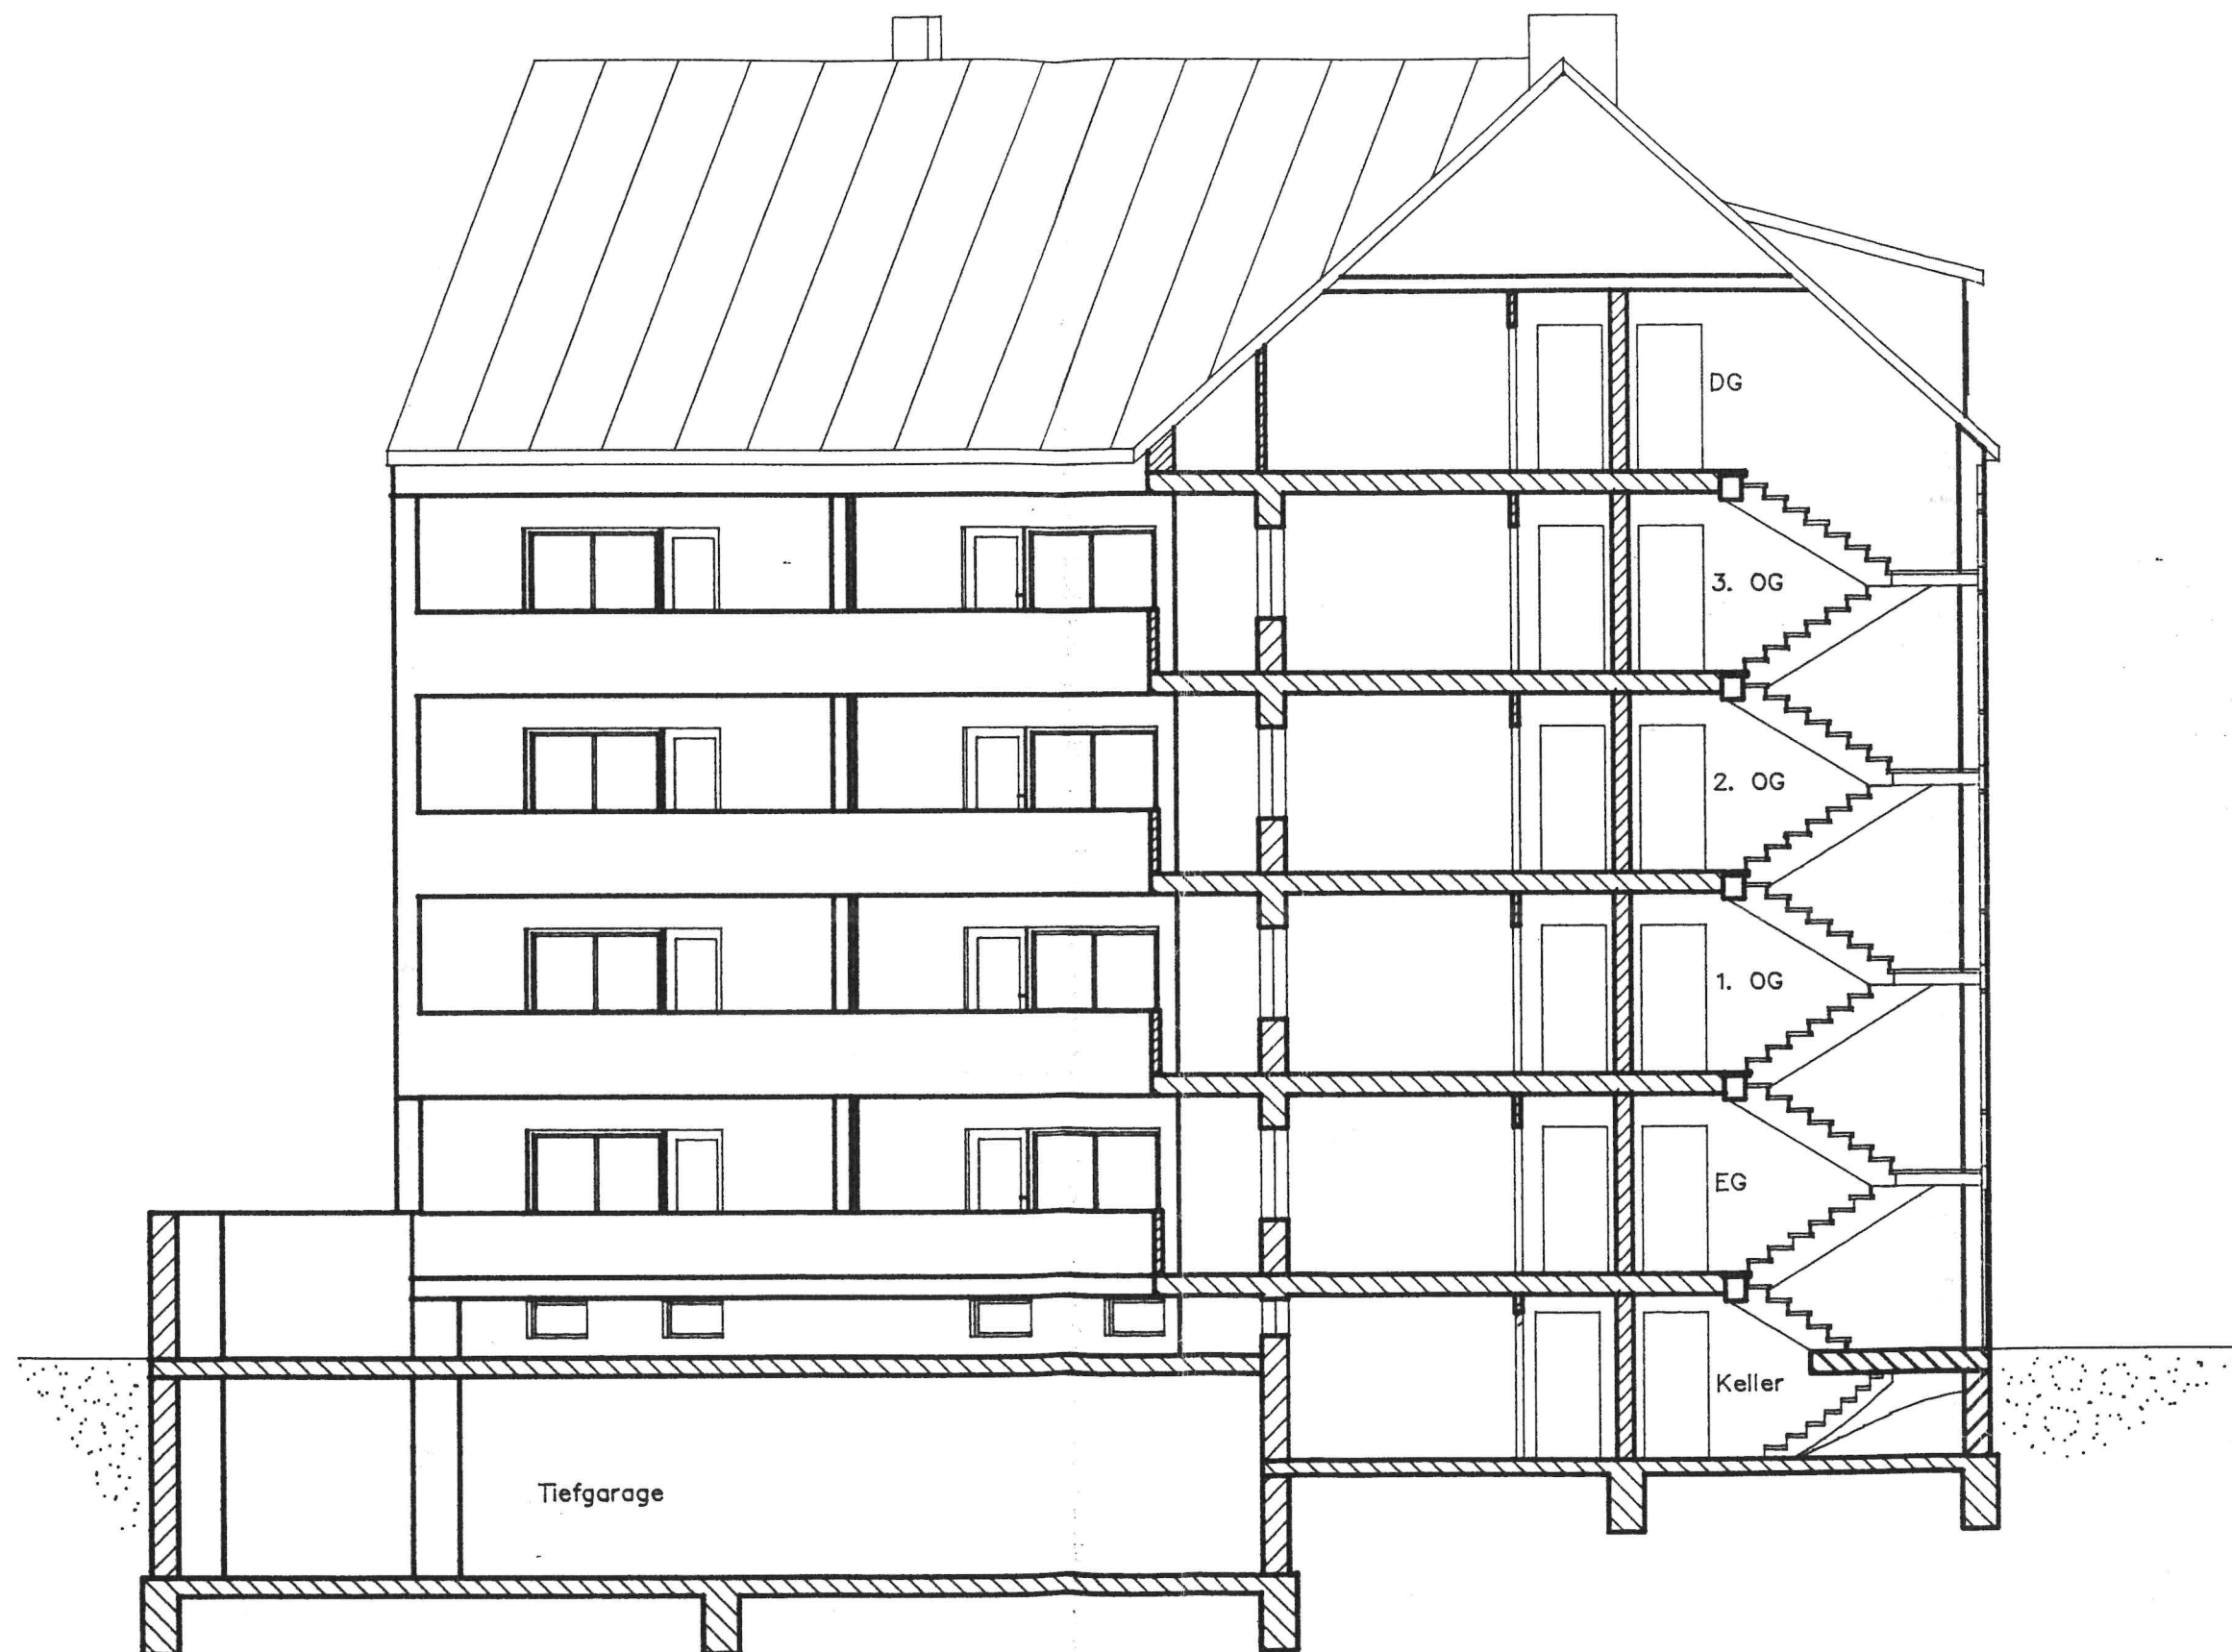

3.00
2.75
2.50
2.00

2.0
2.50
2.70
2.8
2.47
2.75
2.8
2.47
2.75
2.8
2.47
2.75
2.8
2.75
2.75
2.8
2.27
2.55

Bestand
Abgesc
erkläru

Eigentümer: Ludv
Bade
866

Bauort: Fl.Nr
Don
861


Anerkannt:

Grundri
Schnitt
Ansicht

Schnitt

Gefertigt: 20.09.19
Der Planverfasser:

FV

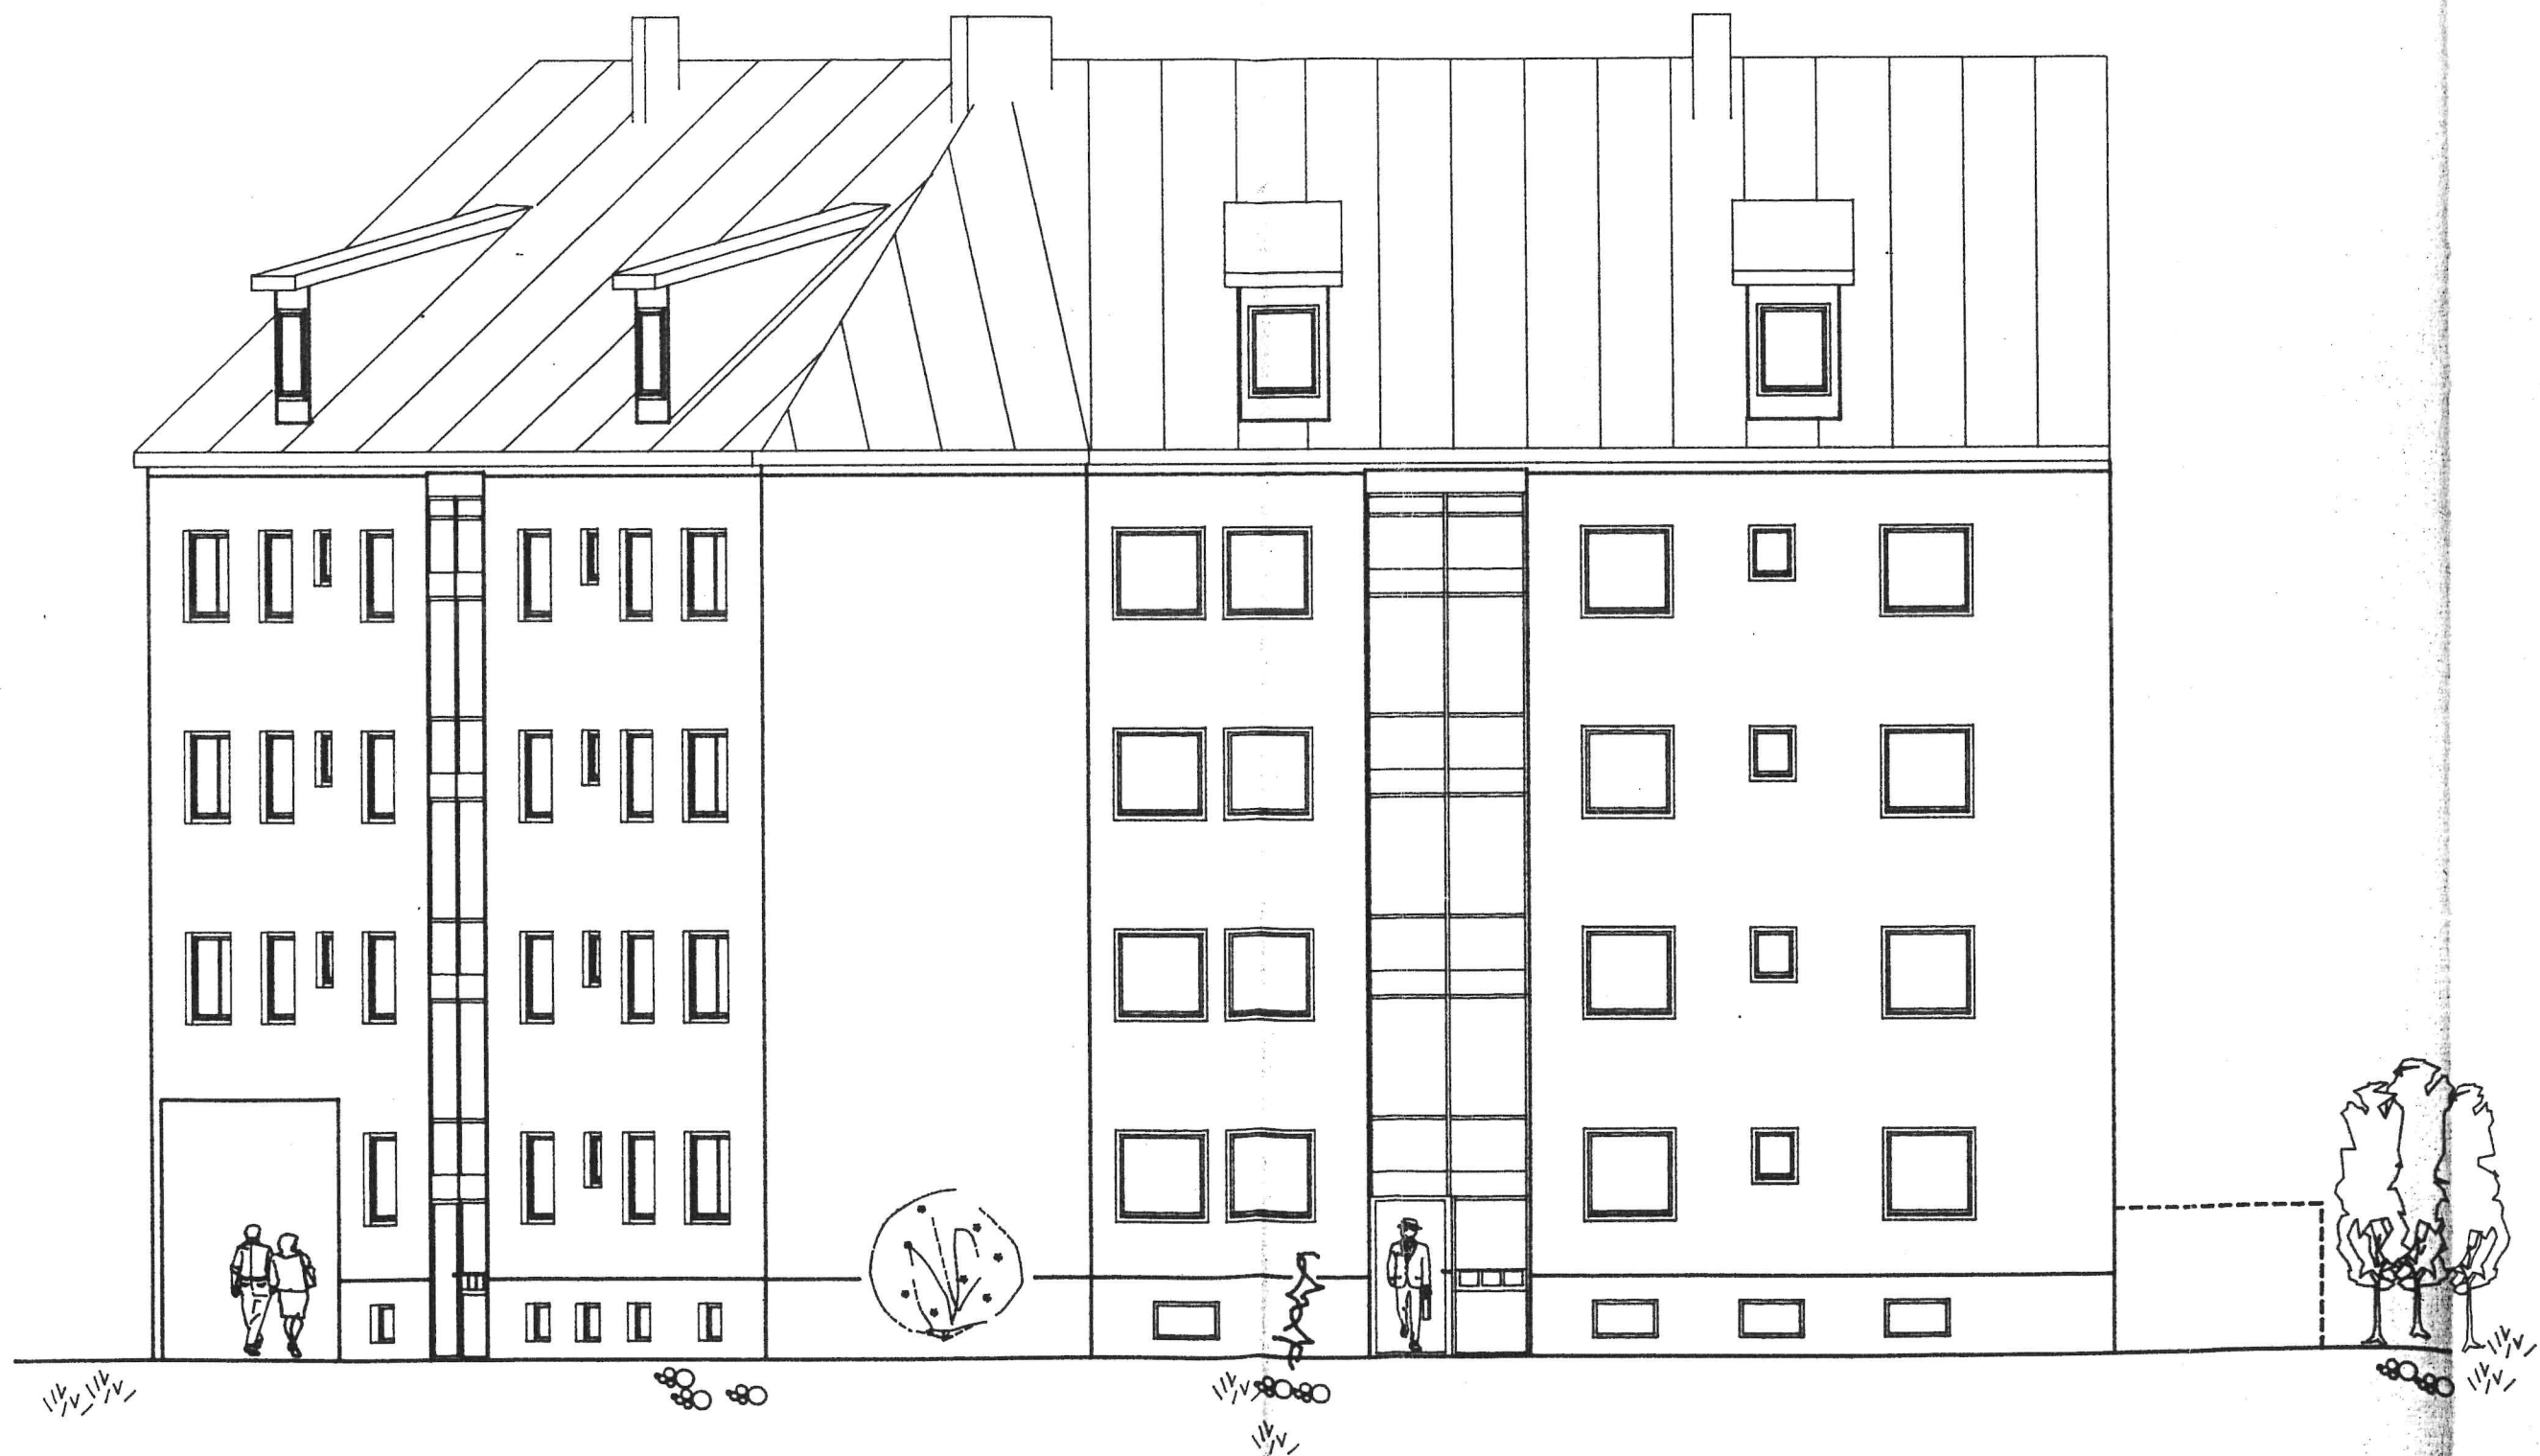

Bestand Abgesch erklärun

Eigentümer: Ludwig
Bc r
8604/

Bauort: Fl.Nr.
Donau
86154

Anerkannt: _____

Grundris
Schnitte
Ansicht

Westans

Gefertigt: 20.09.1994
Der Planverfasser:



Bestand: Abgesch erklärungs

Eigentümer: Ludwig
Bc r
86b47


Bauort: Fl.Nr.
Donau
86154


Anerkannt: _____

Grundris
Schnitte
Ansicht

Südan

Gefertigt: 20.09.1994
Der Planverfasser:

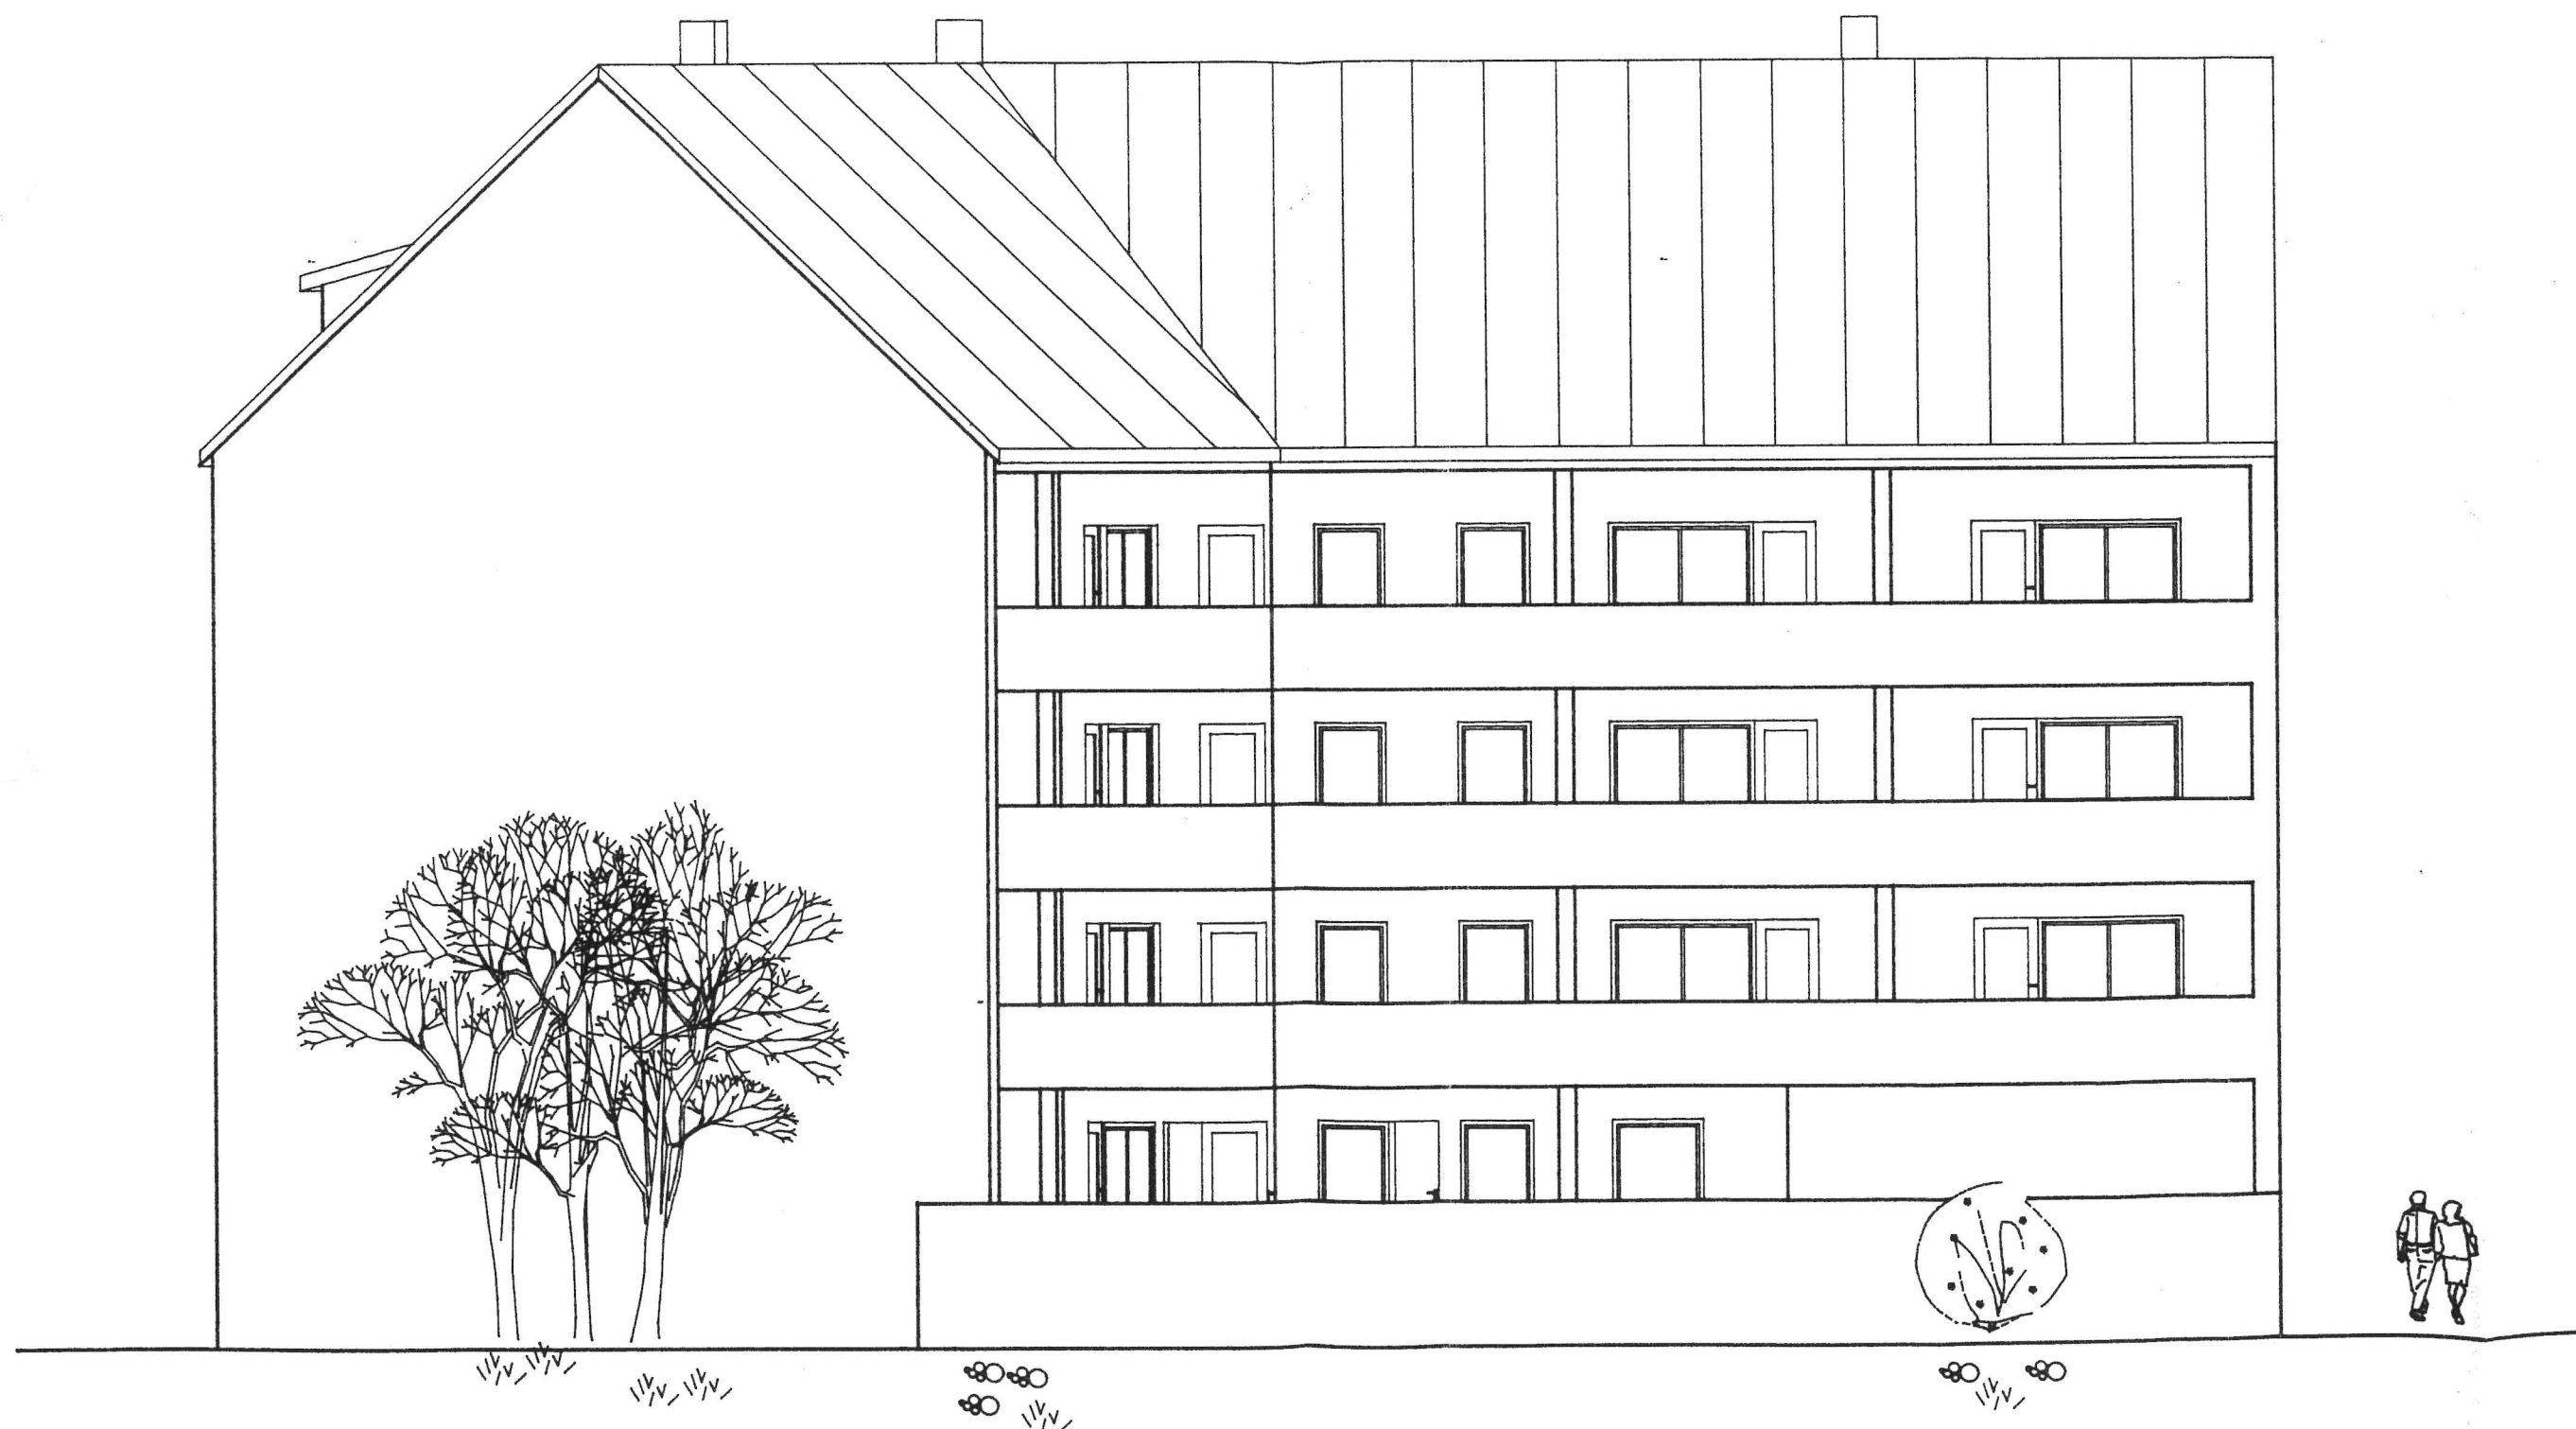

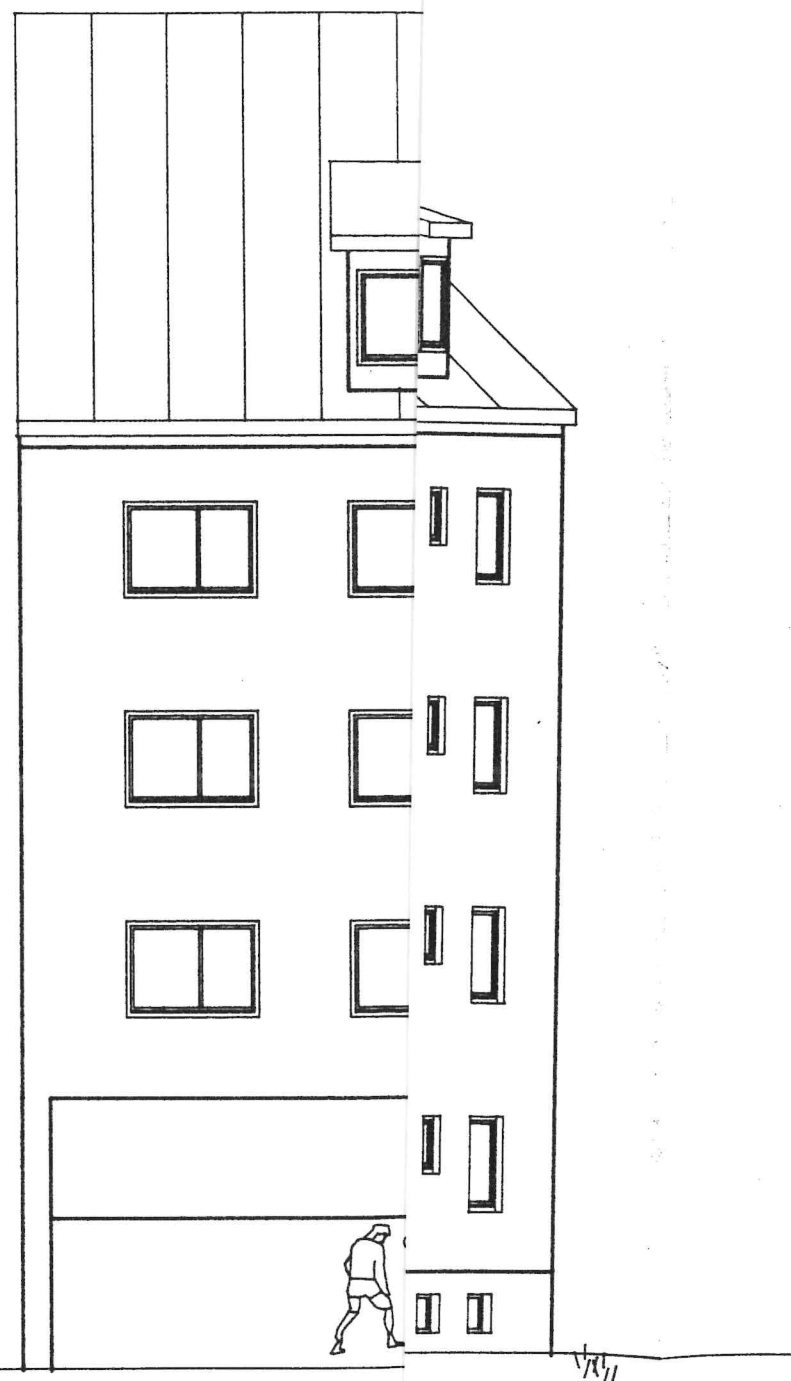

Bestands Abgeschl erklärung

Eigentümer: Ludwig Er
Ba aße
86647 La

Bauort: Fl.Nr. 13
Donauwör
86154 Au

Anerkannt:

Grundriss
Schnitte
Ansich' er

Nordans

Gefertigt: 20.09.1994
Der Planverfasser:



Grundriss Erdgesc

Aufteilungsplan

Antrag auf Abgeschlossenent
zum Anwesen Augsburg,
Griesstrasse 4 / Donauwör


Eigentümer / Ant

Ludwig Ehnle
Badstrasse 2
86647 Lauterbach




Planfertiger

architektur buero fay
raymond fay dipl. ing. (fh) architekt
stichanerstrasse 4 - 86551 aichach
t 08251 877940 - f 08251 6171 - mail@buero.fay.

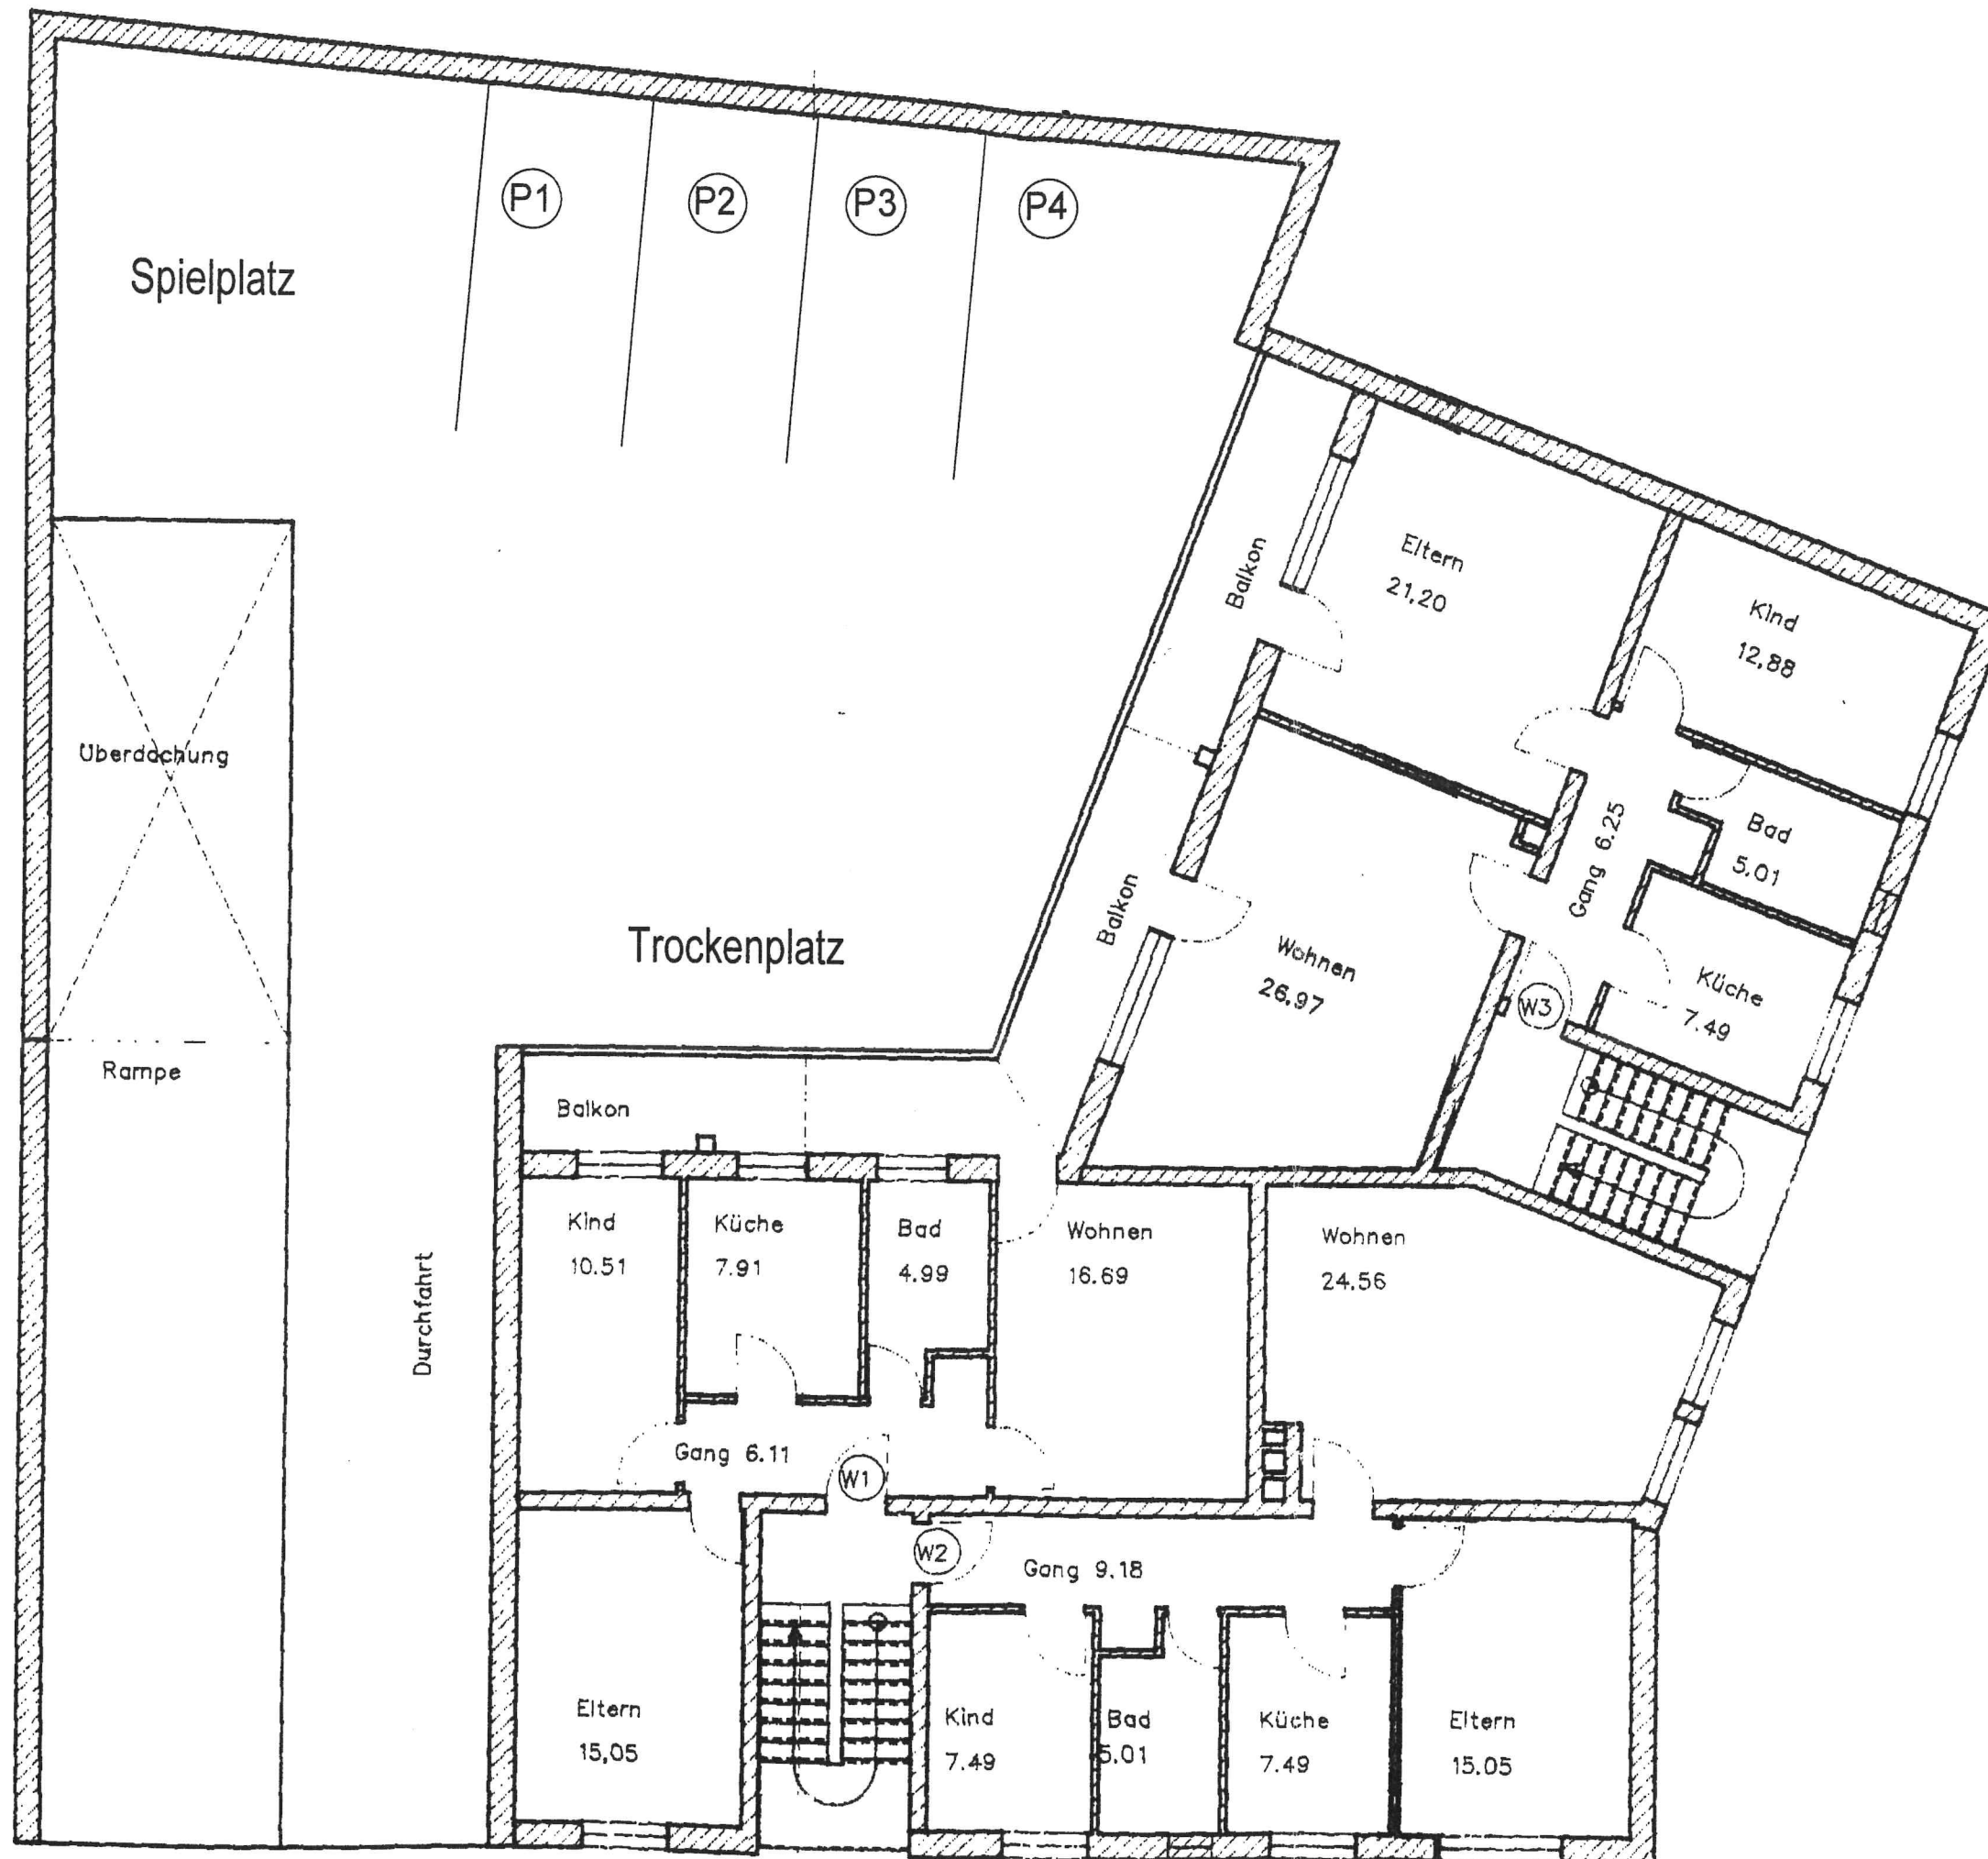

Erdgeschoss

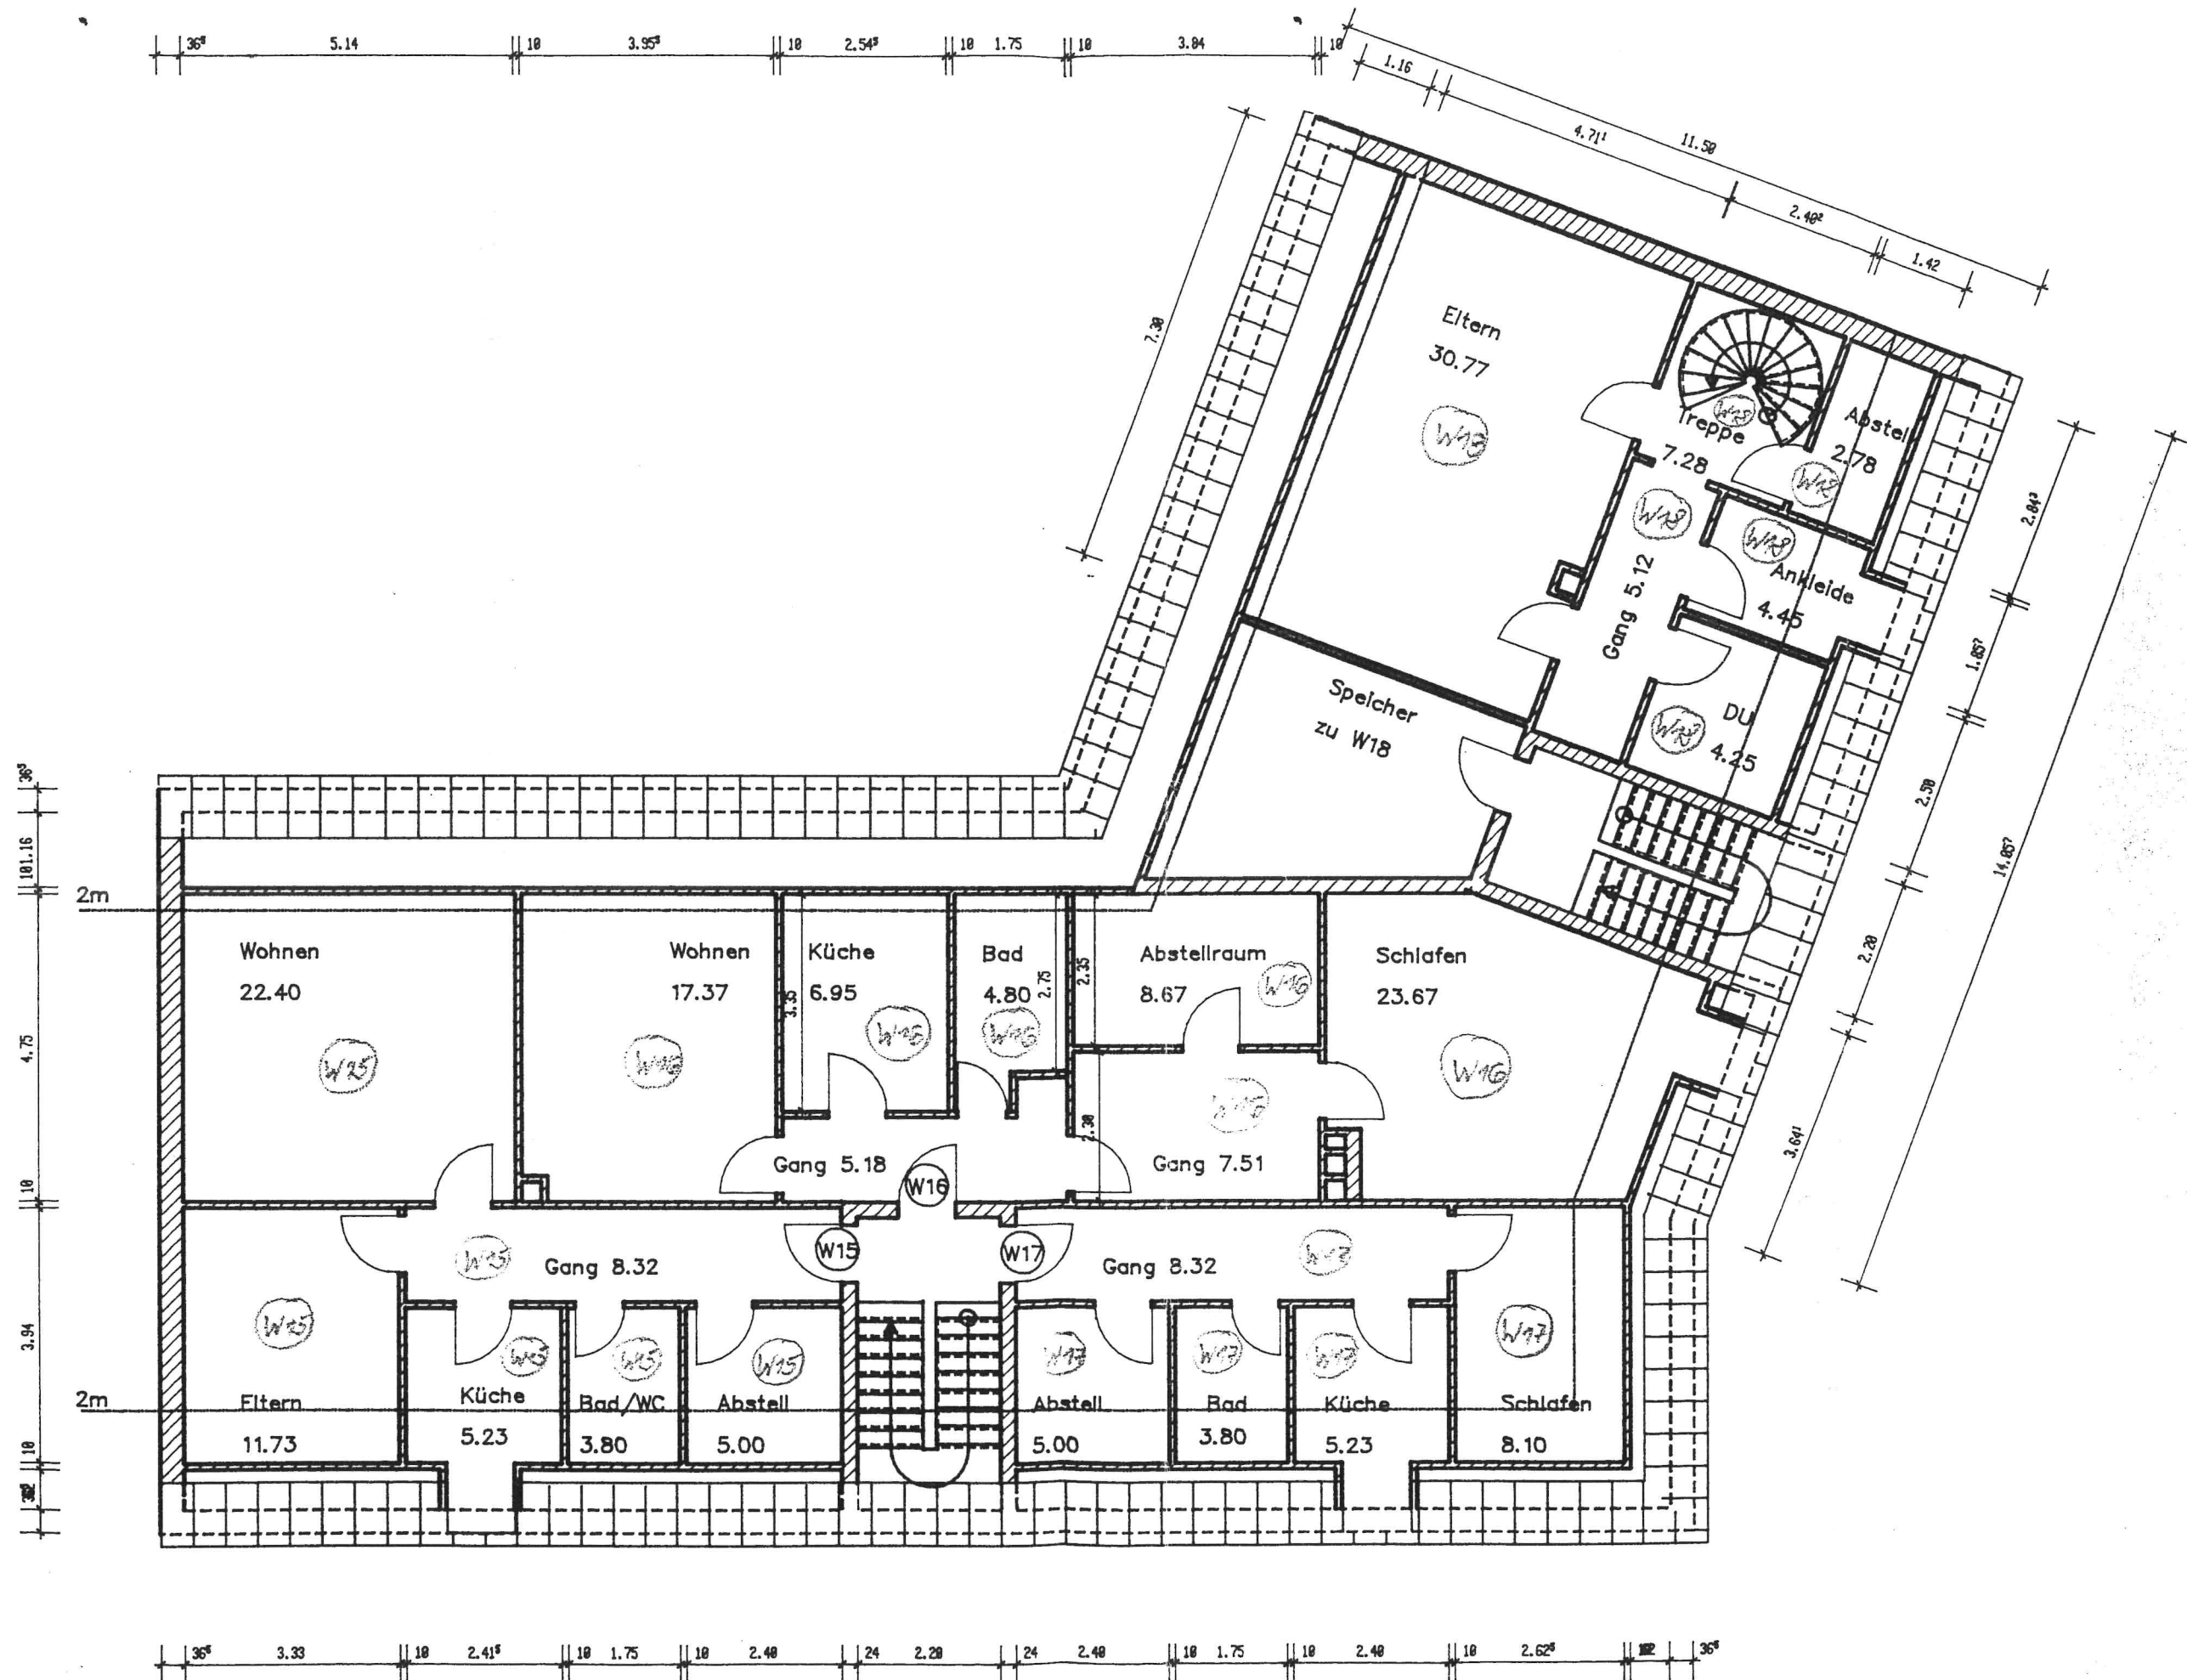

Bestand Abgesch erklärun

Eigentümer: Ludwig
Podst
347

Bauort: Fl.Nr.
Donau
86154






Anerkannt: _____

Grundris Schnitte Ansicht

Dachge

Gefertigt: 20.09.1994
Der Planverfasser:



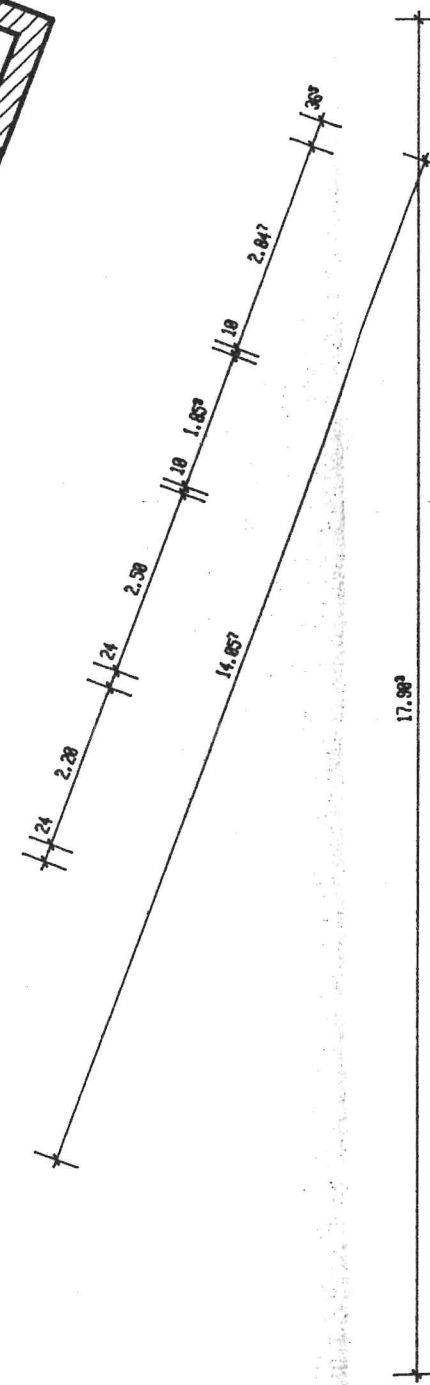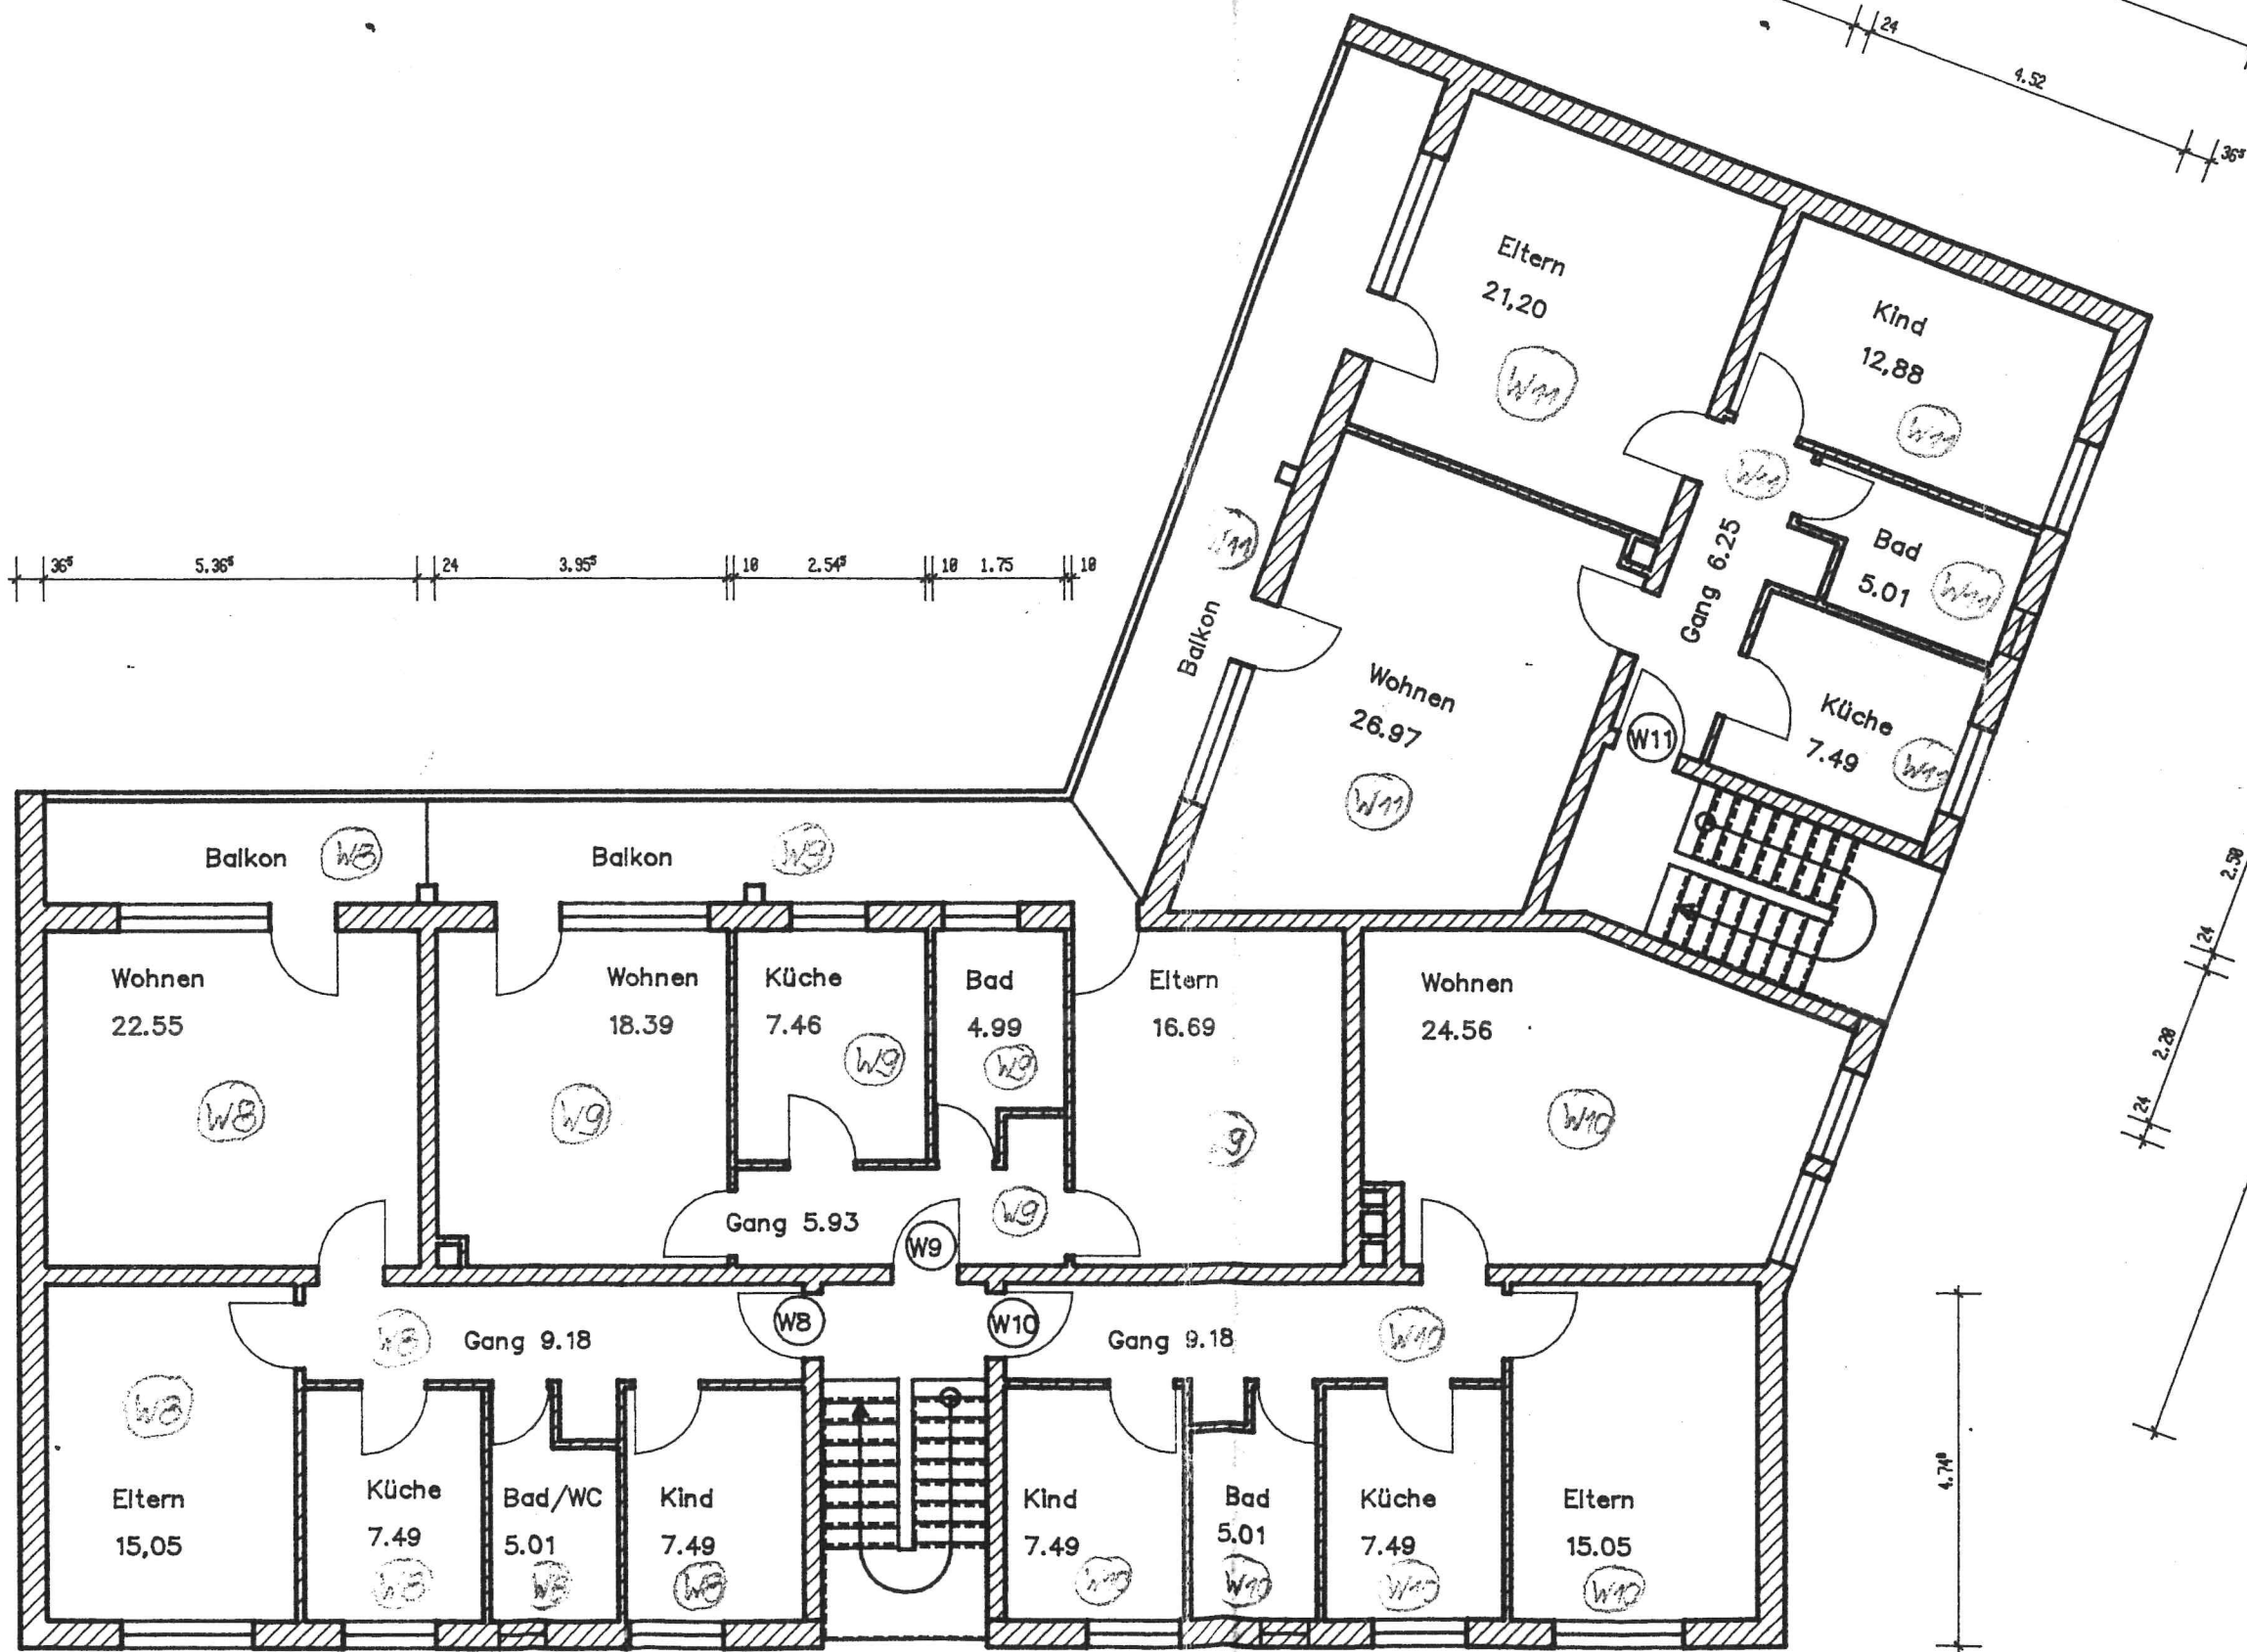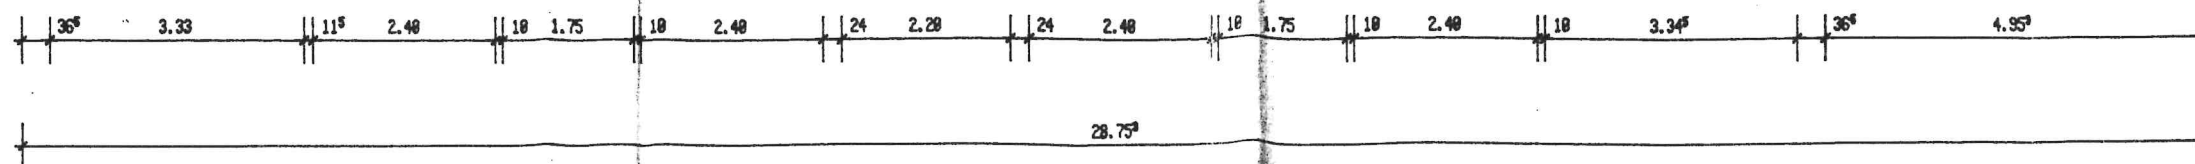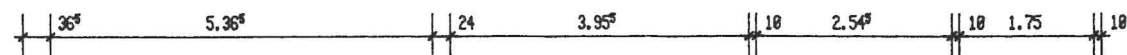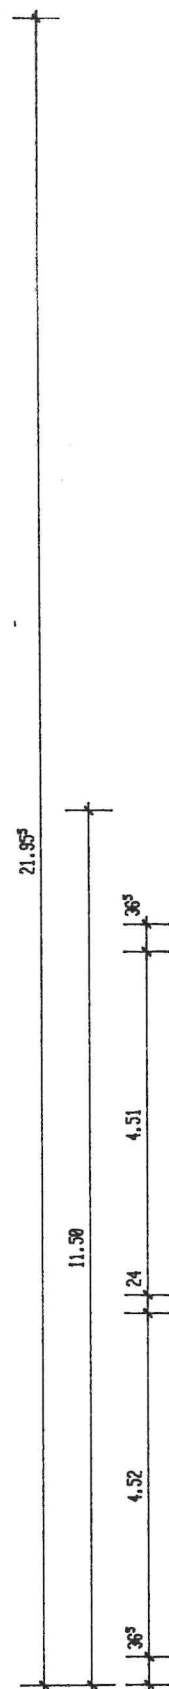

Be
Ab
et

Eigentl


Bauort

Anerka

Gr
Sc
An

Ob

Gefertig
Der Pla

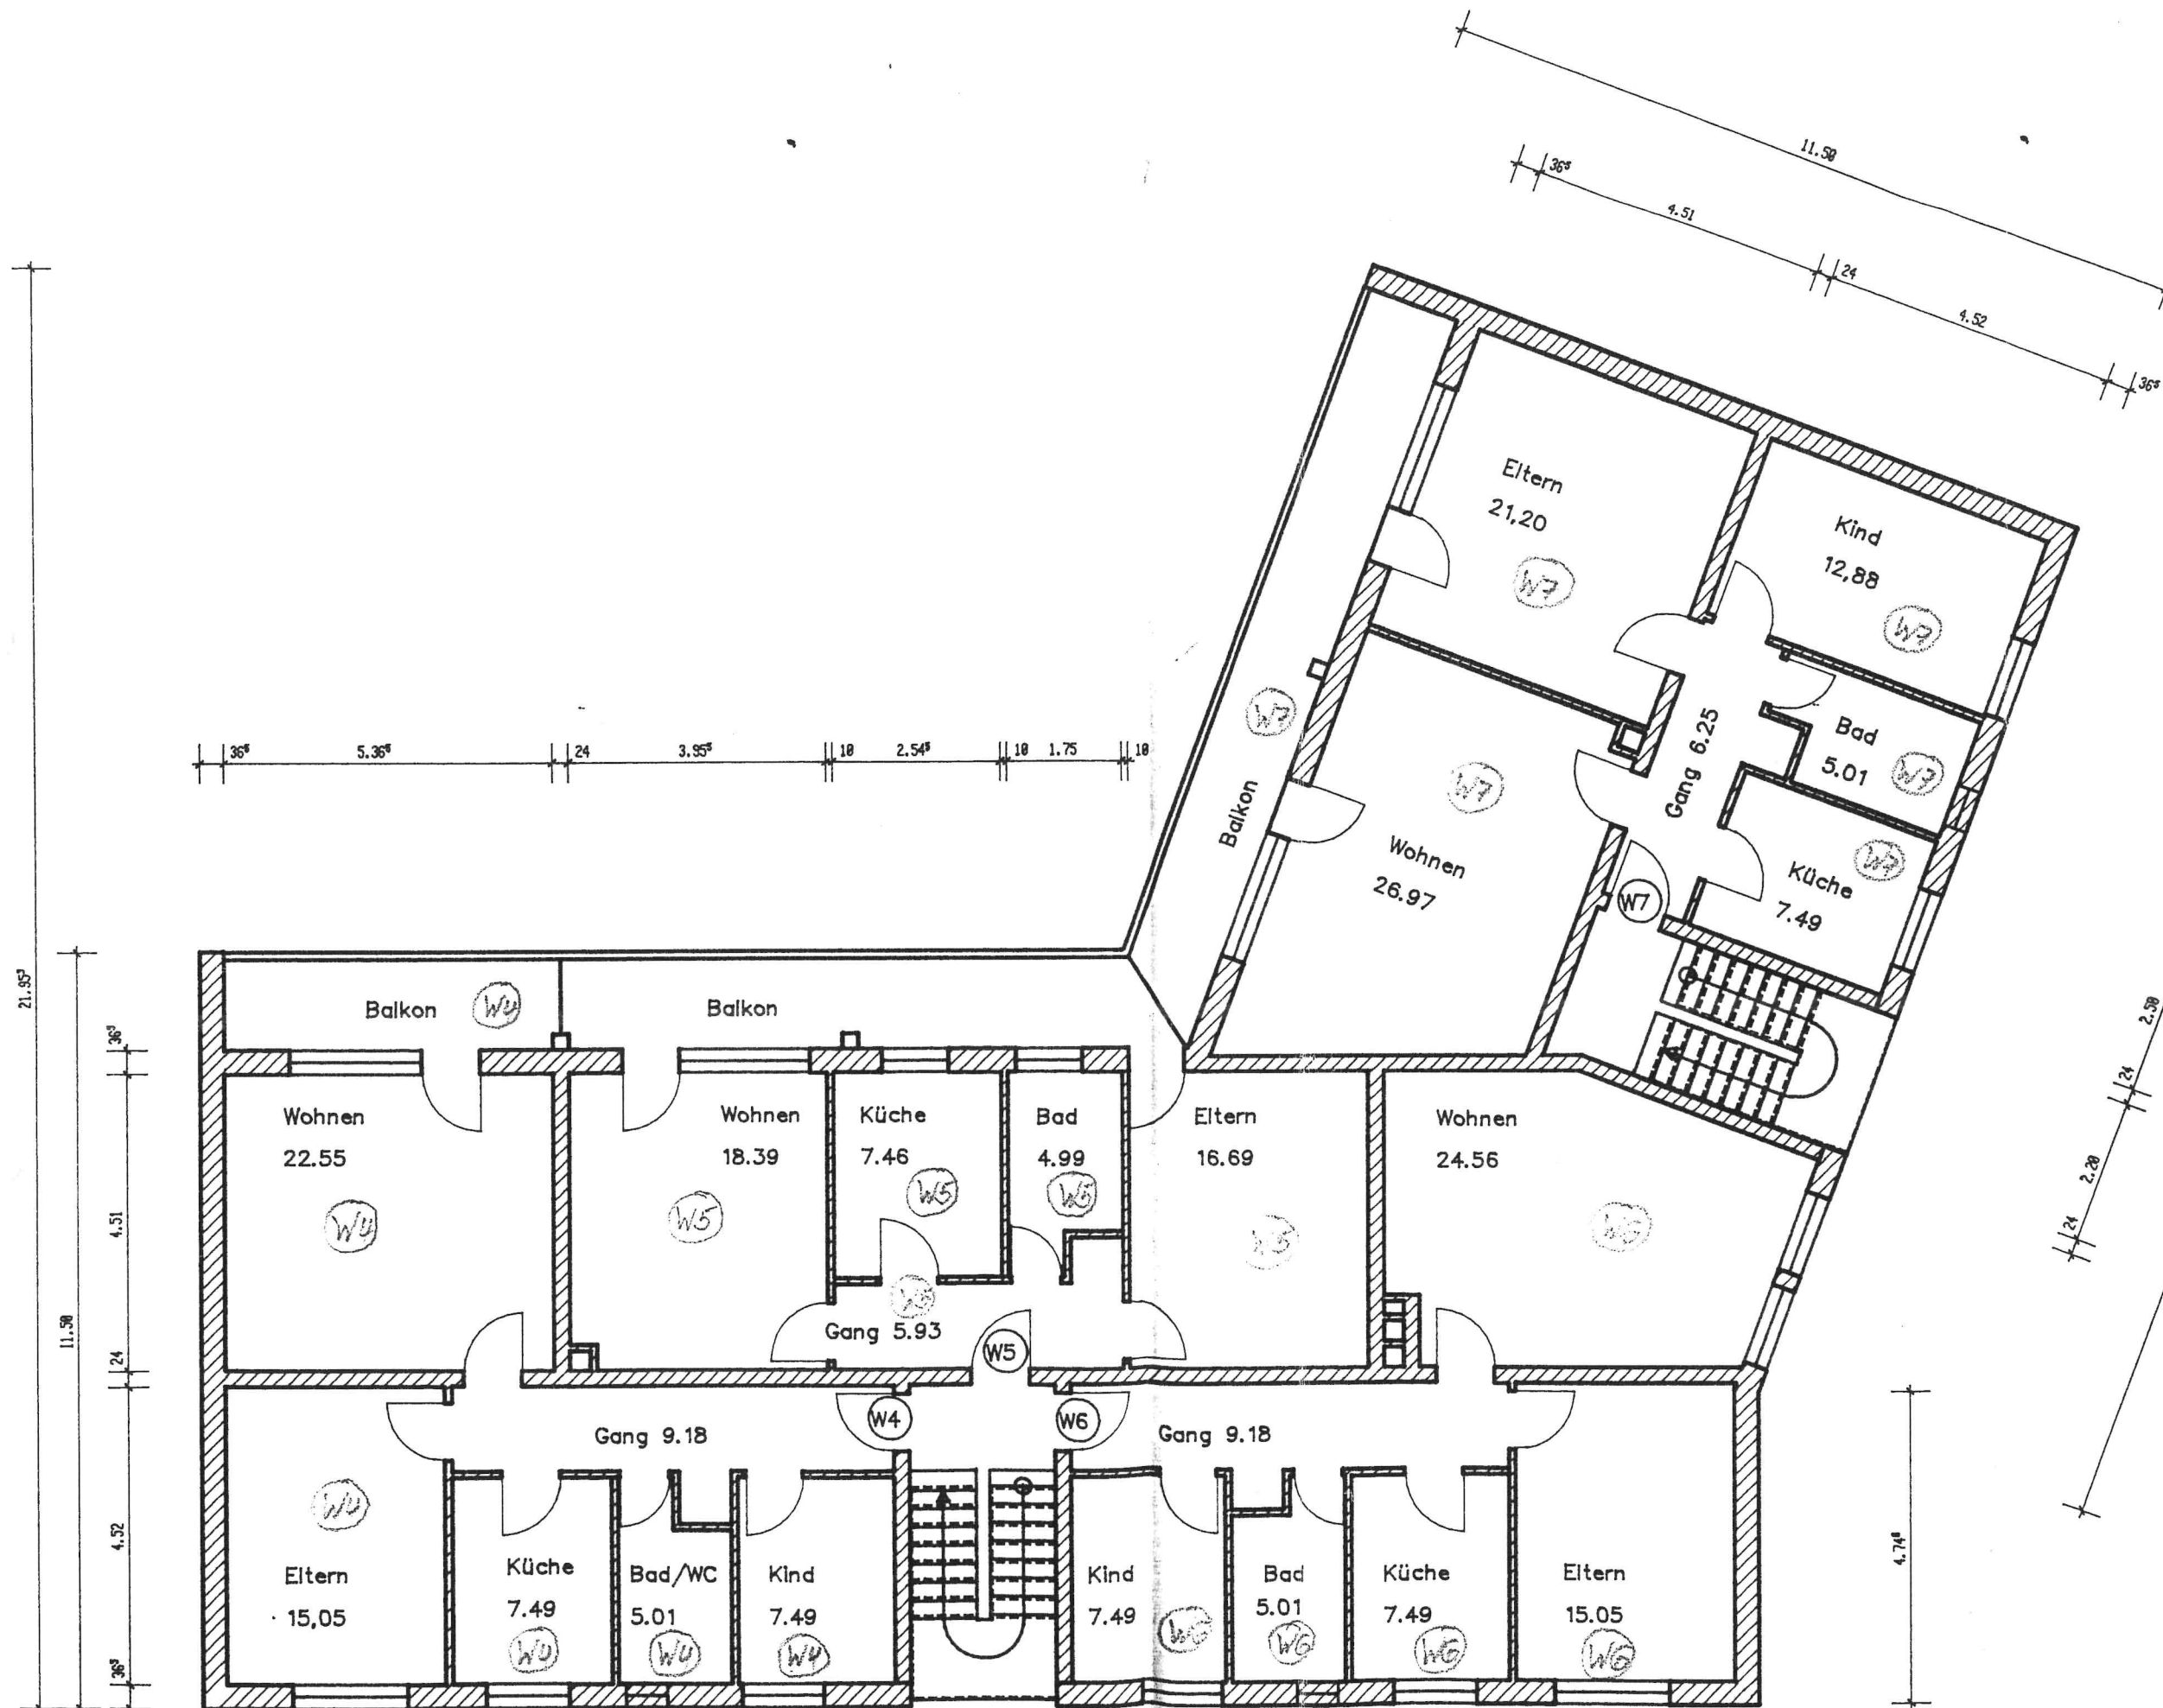

Bestand
Abges
erklär

Eigentümer:

Bauort:

Anerkannt:


Grund
Schni
Ansic

Ober

Gefertigt: 20.0
Der Planverfas



Kellergeschoss

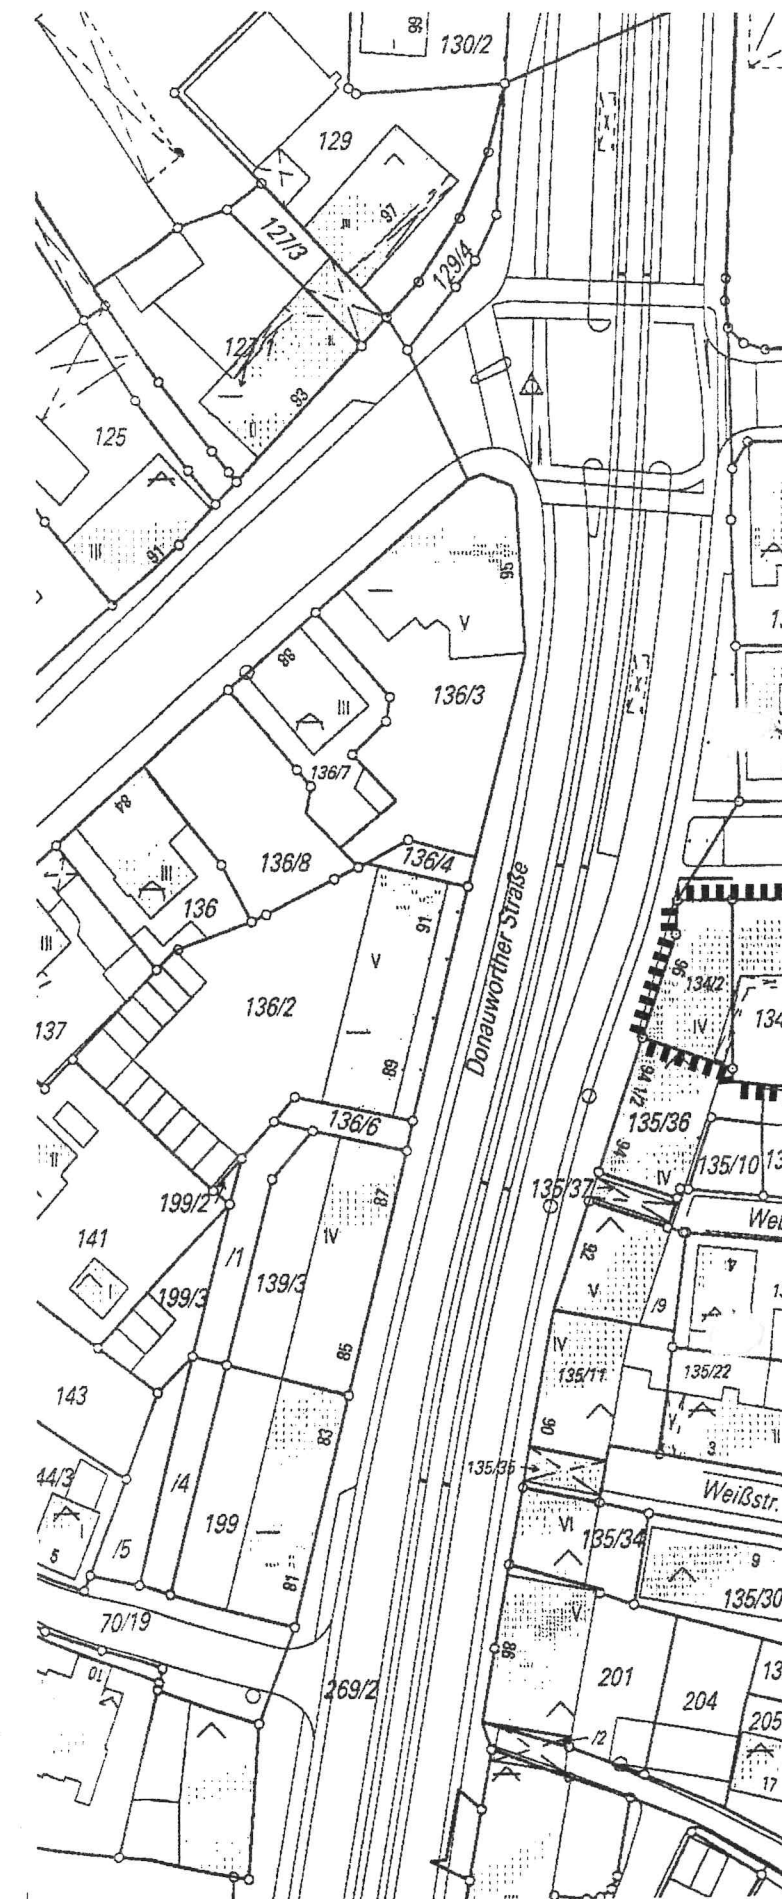

Lageplan M 1:10000



Bestand
Abges
erkläru

Eigentümer: Lu
Ba
86
Bauort: FL
Do
86
Anerkannt:

Grundr
Schnitt
Ansich

Erdrge

Gefertigt: 20.09.1
Der Planverfasser: